
LIST OF DRAWINGS Ground Slab Shop Drawings - Tower B

S. NO.	DRG. NO.	DRAWING TITLE
1	ST-0	List Of Drawings
2	ST-1	Slab Reinforcement X-DIR BOTTOM REINFORCEMENT PLAN
3	ST-2	Slab Reinforcement Y-DIR BOTTOM REINFORCEMENT PLAN
4	ST-3	Slab Reinforcement X-DIRECTION TOP REINFORCEMENT PLAN
5	ST-4	Slab Reinforcement Y-DIRECTION TOP REINFORCEMENT PLAN
6	ST-5	Additional & drop panel Rebar Of Shop Drawing
7	ST-6	Shaft -Slab Reinforcement Shop drawing
8	ST-7	Drop panle Reinforcement Shop drawing
9	ST-8	Stability Ties Reinforcement Plan Layout
10	ST-9	Openings Stiffener Details

CLIENT	AL OMNYAT REAL ESTATE AND TOURISM INVESTMENTS	INFORMATION	NOTES	ARCH.	BAREEQ GENERAL CONTRACTING	Main Contractor	HARMONIC FOR ENGINEERING & GENERAL CONTRACTING
ALOMNYAT COMPANY		Plot Area 2350 m^2		MECH.			
PROJECT NAME		Building Are 2202 m^2		ELEC.		Main Consultant	CREATIVE TOUCH
ALOMNYAT TOWERS		Coverage Area		Civil	CDEC CENTER OF DESIGN & ENGINEERING CONSULTING Prof. Dr. M. EL-ZANATY - Prof. Dr. A. EL-ZANATY		
		Number of Floors 27					
		Plot Number					
		Approved By					

SHEET NAME	
List Of Drawing	
SCALE XX	DATE 19/10/2026
PROJECT NO. K00	REVISION R01

ST-0

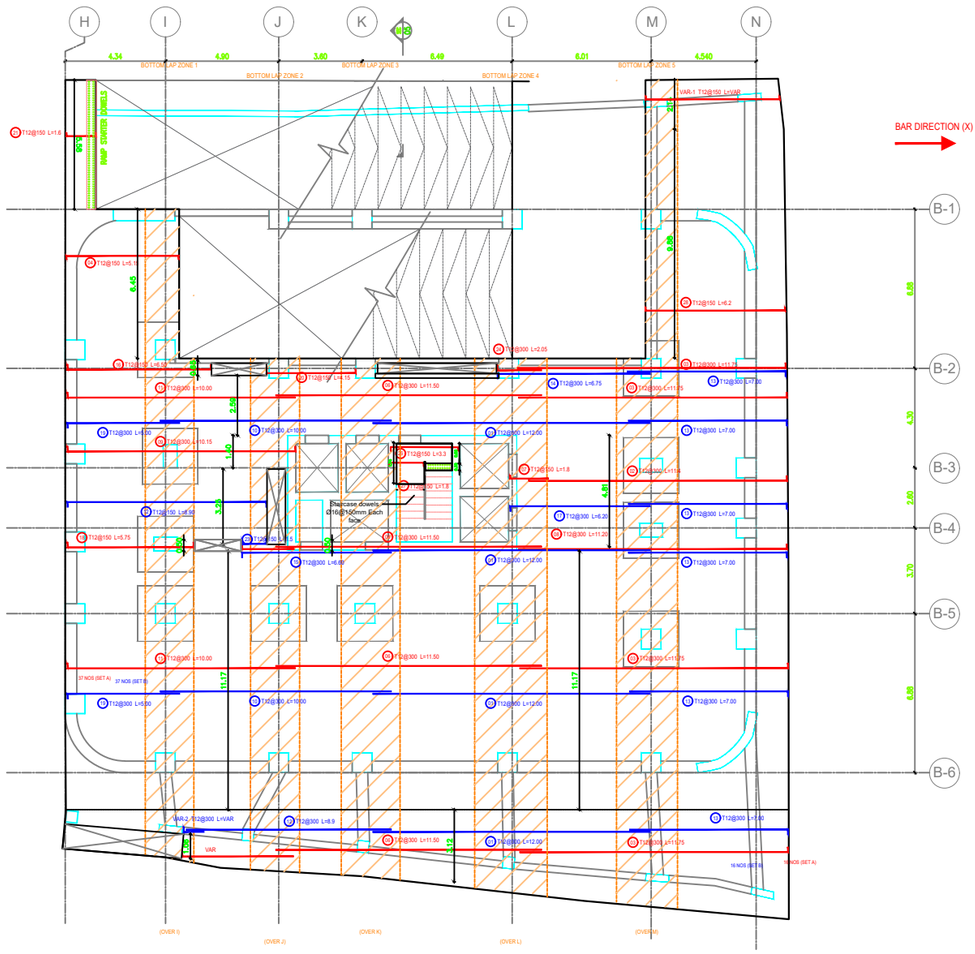

X-DIRECTION BOTTOM REINFORCEMENT PLAN

T12 @ 150 (SET A + SET B @ 300 EACH) - SCALE 1:100

GENERAL NOTES:

1. SLAB REINFORCEMENT: T12 @ 150 mm c/c IN BOTH X & Y DIRECTIONS AT TOP & BOTTOM LAYERS. THIS SHEET SHOWS X-DIRECTION BOTTOM LAYER ONLY.
2. EACH LAYER IS PLACED AS TWO ALTERNATE SETS: SET A (RED) & SET B (BLUE), EACH @ 300 mm -> COMBINED SPACING 150 mm.
3. BOTTOM BARS ARE LAPPED ONLY OVER SUPPORTS (COLUMN GRID LINES (I TO M) / DROP PANELS) INSIDE THE HATCHED "BOTTOM LAP ZONES".
4. LAP SPLICES SHALL BE STAGGERED AND NOT PROVIDED AT THE SAME SECTION: SET A & SET B LAPS ARE SEPARATED BY >= 800 mm.
5. LAP SPLICE LENGTH FOR ALL Ø12 mm BARS = 800 mm MINIMUM. LAPS LONGER THAN 800 mm SUIT THE 12 m STOCK - DO NOT CUT BARS.
6. ALL BARS ENDING AT SLAB EDGES & OPENINGS HAVE A 150 mm HOOK (BOTTOM BARS TURNED UP). END COVER = 25 mm TYP., 50 mm WHERE THE BAR ENDS ON A BEAM / COLUMN.
7. NO REINFORCEMENT INSIDE LIFT CORE, STAIR, SLAB OPENINGS OR RAMP. AT THE CORE, BARS RUN THROUGH THE WALLS AND STOP AT THE INNER FACE (25 mm COVER + 150 HOOK).
8. VAR BARS: ONLY AT THE INCLINED SLAB EDGES; SHOWN BY A TYPICAL BAR PER ZONE - CUT LENGTHS IN THE VAR SCHEDULE.
9. SLAB DIMENSIONS & OPENINGS ARE AS PER STRUCTURAL PLAN. VERIFY ON SITE BEFORE CUTTING.
10. TRIMMER BARS AROUND OPENINGS AND RAMP REINFORCEMENT ARE AS PER STRUCTURAL DETAILS (NOT PART OF THIS SCHEDULE).
11. BAR LENGTHS IN THE SCHEDULE ARE CUTTING LENGTHS (INCLUDING HOOKS), IN METRES.

LEGEND

- SET A BAR (T12@300)
- SET B BAR (T12@300)
- PERMITTED LAP ZONE (OVER SUPPORTS)
- DISTRIBUTION RANGE OF BAR GROUP
- T12@300 L=11.75 : BAR MARK / SPACING / CUT LENGTH
- TYPICAL LAP & END DETAIL (N.T.S.)



BAR BENDING SCHEDULE - X-DIRECTION BOTTOM LAYER

SLAB REINFORCEMENT X-DIR BOTTOM MESH (SETS A & B)

NAME	BAR MARK	No.	Ø SIZE	LENGTH OF BAR (m)	SHAPE (m)
	01	58	Ø12	12.00	12.00
	02	16	Ø12	11.4	0.15 11.25 0.15
	03	59	Ø12	11.75	0.15 11.60 0.15
	04	43	Ø12	5.15	0.15 4.85 0.15
	05				
	06	58	Ø12	11.50	11.50
	07	16	Ø12	1.8	0.15 1.65
	08	1	Ø12	11.85	0.15 11.7
	09	9	Ø12	10.15	0.15 9.85 0.15
	10	45	Ø12	10.00	10.00
	11	46	Ø12	10.00	0.15 9.85
	12	22	Ø12	8.90	0.15 8.60 0.15
	13	68	Ø12	7.00	6.85 0.15
	14	2	Ø12	6.75	0.15 6.60
	15	1	Ø12	6.60	0.15 6.45
	16	4	Ø12	6.50	0.15 6.20 0.15
	17	16	Ø12	6.20	0.15 6.05
	18	2	Ø12	5.75	0.15 5.45 0.15
	19	46	Ø12	5.00	0.15 4.85
	20	3	Ø12	4.15	0.15 4.65 0.15
	21	38	Ø12	1.57	0.15 1.27 0.15
	22				
	23	1	Ø12	1.5	0.15 1.2
	24	1	Ø12	2.05	0.15 1.90
	25				
	VAR	VAR	Ø12	VAR	0.15 VAR
	26	6	Ø12	3.3	0.15 3 0.15
	27	4	Ø12	1.77	0.15 1.47 0.15

CLIENT	AL OMNYAT REAL ESTATE AND TOURISM INVESTMENTS
ALOMNYAT COMPANY	
PROJECT NAME	
ALOMNYAT TOWERS	


INFORMATION	NOTES
Plot Area 2350 m^2	
Building Are 2202 m^2	
Coverage Area	
Number of Floors 27	
Plot Number	
Approved By	

ARCH.	BAREEQ GENERAL CONTRACTING
MECH.	
ELEC.	
Civil	CDEC CENTER OF DESIGN & ENGINEERING CONSULTING Prof. Dr. M. EL-ZANATY - Prof. Dr. A. EL-ZANATY

Main Contractor	HARMONIC FOR ENGINEERING & GENERAL CONTRACTING
Main Consultant	CREATIVE TOUCH FOR INTERIOR ARCHITECTURE & ENGINEERING

SHEET NAME	
X-DIR BOTTOM REINFORCEMENT PLAN Shop Drawing	
SCALE XX	DATE 19/10/2026
PROJECT NO. K00	REVISION R01

ST-1

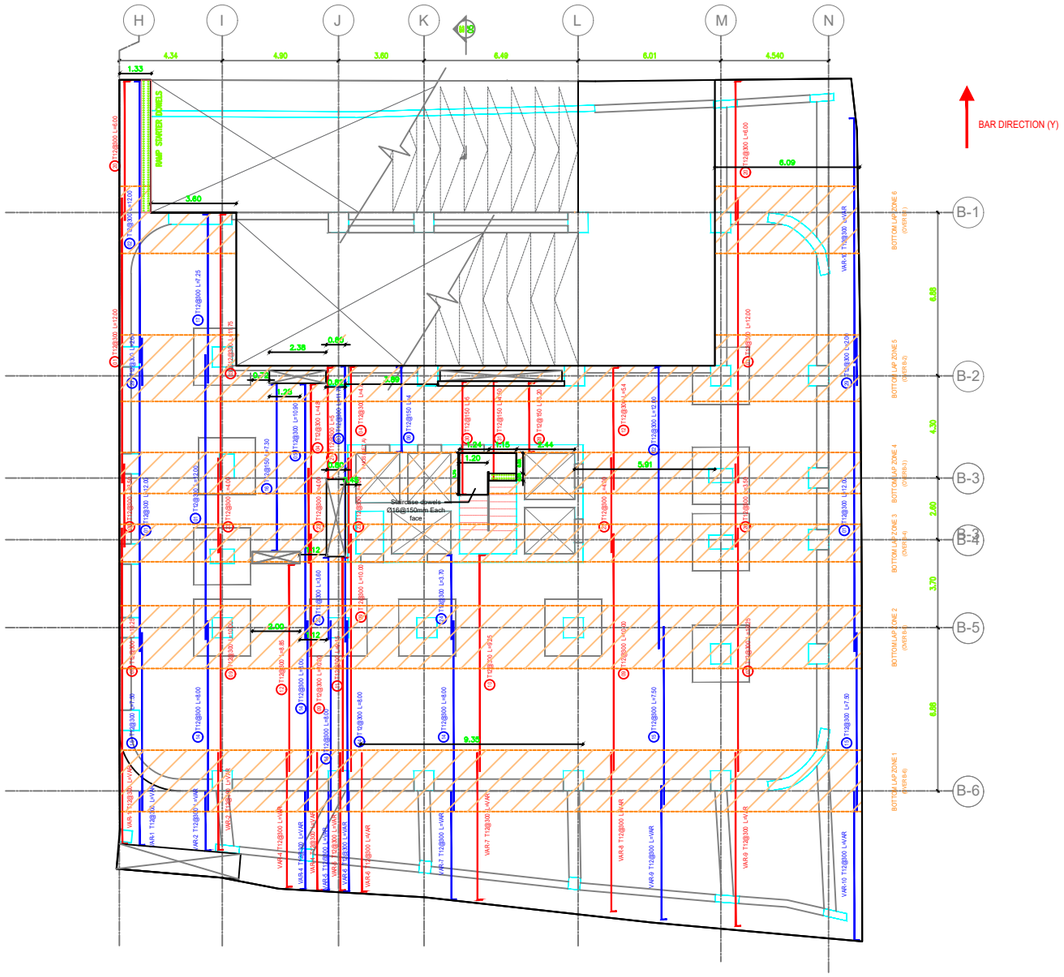

Y-DIRECTION BOTTOM REINFORCEMENT PLAN

T12 @ 150 (SET A + SET B @ 300 EACH) - SCALE 1:100

BAR BENDING SCHEDULE - Y-DIRECTION BOTTOM LAYER

SLAB REINFORCEMENT Y-DIR BOTTOM MESH (SETS A & B)

NAME	BAR MARK	No.	Ø SIZE	LENGTH OF BAR (m)	SHAPE (m)
	01	62	Ø12	12.00	12.00
	02	24	Ø12	12.00	0.15 11.85 0.15
	03	13	Ø12	11.75	0.15 11.60 0.15
	04	5	Ø12	4.75	0.15 4.6
	05	4	Ø12	10.90	0.15 10.75 0.15
	06	26	Ø12	3.87	0.15 3.57 0.15
	07	25	Ø12	10.25	10.25
	08				
	09	37	Ø12	10.00	10.00
	10	31	Ø12	9.25	0.15 9.10
	11	2	Ø12	9.15	0.15 9.00 0.15
	12	26	Ø12	8.85	0.15 8.7
	13				
	14	48	Ø12	8.00	8.00
	15	45	Ø12	7.50	7.50
	16	9	Ø12	7.30	0.15 7.00 0.15
	17	12	Ø12	7.25	0.15 7.10
	18				
	19				
	20	25	Ø12	6.00	0.15 5.85
	21	6	Ø12	5	0.15 4.7 0.15
	22				
	23	37	Ø12	4.00	4.00
	24	31	Ø12	3.70	0.15 3.55
	25	3	Ø12	3.60	0.15 3.45
	26	25	Ø12	3.50	3.50
	27				
	28	32	Ø12	3.20	0.15 2.90 0.15
	29	25	Ø12	2.00	2.00
	VAR	VAR	Ø12	VAR	0.15
	30	8	Ø12	5	0.15 4.7 0.15
	31	8	Ø12	4.5	0.15 4.3 0.15


GENERAL NOTES:

1. SLAB REINFORCEMENT: T12 @ 150 mm c/c IN BOTH X & Y DIRECTIONS AT TOP & BOTTOM LAYERS. THIS SHEET SHOWS Y-DIRECTION BOTTOM LAYER ONLY.
2. EACH LAYER IS PLACED AS TWO ALTERNATE SETS: SET A (RED) & SET B (BLUE), EACH @ 300 mm -> COMBINED SPACING 150 mm.
3. BOTTOM BARS ARE LAPPED ONLY OVER SUPPORTS (B-GRID LINES (B-1 TO B-6) / DROP PANELS) INSIDE THE HATCHED "BOTTOM LAP ZONES".
4. LAP SPLICES SHALL BE STAGGERED AND NOT PROVIDED AT THE SAME SECTION: SET A & SET B LAPS ARE SEPARATED BY >= 800 mm.
5. LAP SPLICE LENGTH FOR ALL Ø12 mm BARS = 800 mm MINIMUM. LAPS LONGER THAN 800 mm SUIT THE 12 m STOCK - DO NOT CUT BARS.
6. ALL BARS ENDING AT SLAB EDGES & OPENINGS HAVE A 150 mm HOOK (BOTTOM BARS TURNED UP). END COVER = 25 mm TYP., 50 mm WHERE THE BAR ENDS ON A BEAM / COLUMN.
7. NO REINFORCEMENT INSIDE LIFT CORE, STAIR, SLAB OPENINGS OR RAMP. AT THE CORE, BARS RUN THROUGH THE WALLS AND STOP AT THE INNER FACE (25 mm COVER + 150 HOOK).
8. VAR BARS: ONLY AT THE INCLINED SLAB EDGES; SHOWN BY A TYPICAL BAR PER ZONE - CUT LENGTHS IN THE VAR SCHEDULE.
9. SLAB DIMENSIONS & OPENINGS ARE AS PER STRUCTURAL PLAN. VERIFY ON SITE BEFORE CUTTING.
10. TRIMMER BARS AROUND OPENINGS AND RAMP REINFORCEMENT ARE AS PER STRUCTURAL DETAILS (NOT PART OF THIS SCHEDULE).
11. BAR LENGTHS IN THE SCHEDULE ARE CUTTING LENGTHS (INCLUDING HOOKS), IN METRES.

LEGEND

- SET A BAR (T12@300)
- SET B BAR (T12@300)
- PERMITTED LAP ZONE (OVER SUPPORTS)
- DISTRIBUTION RANGE OF BAR GROUP
- T12@300 L=11.75 : BAR MARK / SPACING / CUT LENGTH

TYPICAL LAP & END DETAIL (N.T.S.)

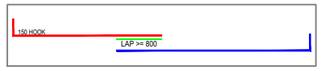

CLIENT	
ALOMNYAT COMPANY	
PROJECT NAME	
ALOMNYAT TOWERS	

AL OMNYAT
REAL ESTATE AND TOURISM INVESTMENTS

INFORMATION	NOTES
Plot Area 2350 m^2	
Building Are 2202 m^2	
Coverage Area	
Number of Floors 27	
Plot Number	
Approved By	

ARCH.	BAREEQ GENERAL CONTRACTING
MECH.	
ELEC.	
Civil	CDEC CENTER OF DESIGN & ENGINEERING CONSULTING Prof. Dr. M. EL-ZANATY - Prof. Dr. A. EL-ZANATY Administration Building N0 (2) Spring Valley(Kanawy)-AL-Motamayaz district 6 th of October-Giza


Main Contractor	HARMONIC FOR ENGINEERING & GENERAL CONTRACTING
Main Consultant	CREATIVE TOUCH FOR ENGINEERING CONSULTING

SHEET NAME

Y-DIR BOTTOM REINFORCEMENT PLAN
Shop Drawing

SCALE	DATE
XX	19/10/2026

PROJECT NO.	REVISION	
K00	R01	ST-2

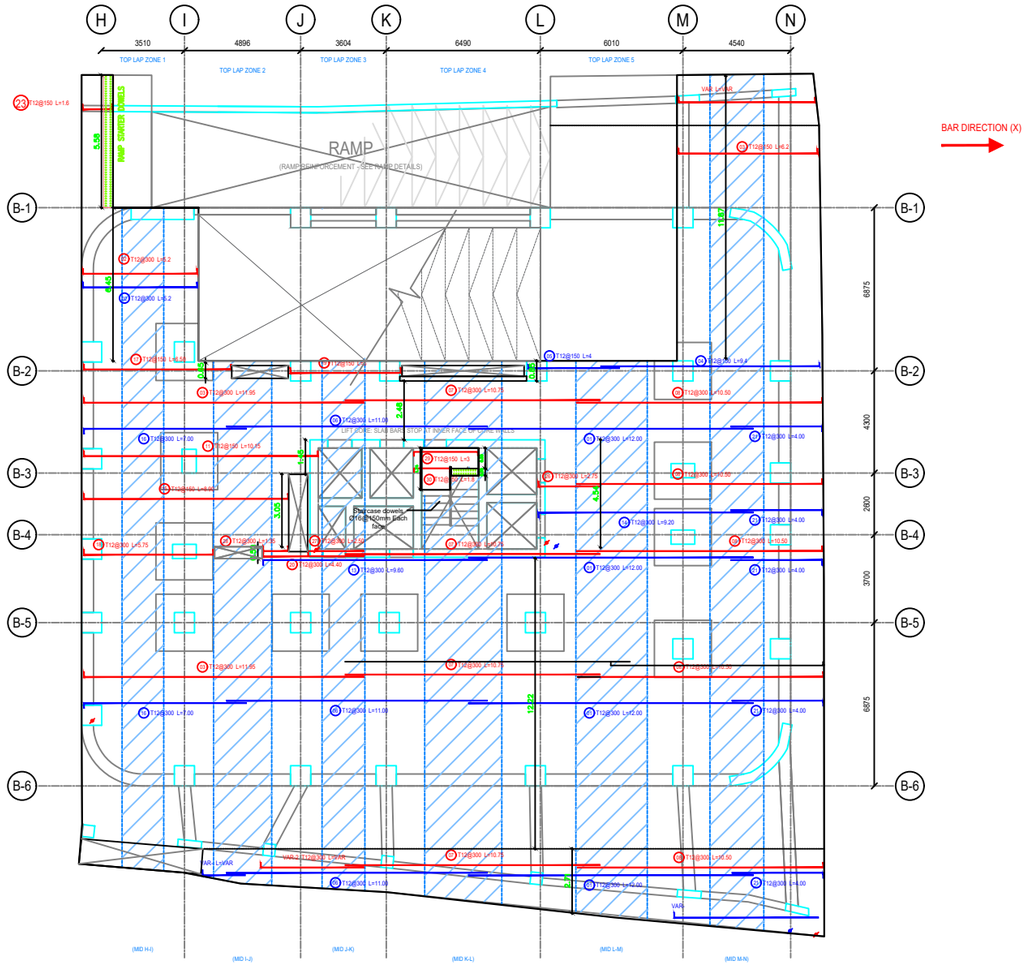

X-DIRECTION TOP REINFORCEMENT PLAN

T12 @ 150 (SET A + SET B @ 300 EACH) - SCALE 1:100

BAR BENDING SCHEDULE - X-DIRECTION TOP LAYER

SLAB REINFORCEMENT X-DIR TOP MESH (SETS A & B)

NAME	BAR MARK	No.	Ø SIZE	LENGTH OF BAR (m)	SHAPE (m)
	01	60	Ø12	12.00	12.00
	02	43	Ø12	5.1	4.8 (0.15 / 0.15)
	03	72	Ø12	6.2	5.9 (0.15 / 0.15)
	04	2	Ø12	9.6	9.45 (0.15)
	05	2	Ø12	4	3.85 (0.15)
	06	54	Ø12	11.00	11.00
	07	56	Ø12	10.75	10.75
	08	75	Ø12	10.50	10.35 (0.15)
	09				
	10				
	11	10	Ø12	10.15	9.85 (0.15 / 0.15)
	12				
	13	1	Ø12	9.60	9.45 (0.15)
	14	16	Ø12	9.20	9.05 (0.15)
	15	21	Ø12	8.90	8.60 (0.15 / 0.15)
	16	49	Ø12	7.00	6.85 (0.15)
	17	4	Ø12	6.50	6.20 (0.15 / 0.15)
	18	2	Ø12	5.75	5.45 (0.15 / 0.15)
	19	4	Ø12	4.90	4.60 (0.15 / 0.15)
	20	1	Ø12	4.4	4.25 (0.15)
	21	76	Ø12	4.00	3.85 (0.15 / 0.15)
	22				
	23	37	Ø12	1.6	1.3 (0.15 / 0.15)
	24				2.85
	25				
	26	15	Ø12	2.75	2.60 (0.15)
	27	1	Ø12	2.50	2.35 (0.15)
	28	1	Ø12	1.32	1.05 (0.15 / 0.15)
	29	6	Ø12	3	2.7 (0.15 / 0.15)
	30	4	Ø12	1.77	1.47 (0.15 / 0.15)

GENERAL NOTES:

1. SLAB REINFORCEMENT: T12 @ 150 mm c/c IN BOTH X & Y DIRECTIONS AT TOP & BOTTOM LAYERS. THIS SHEET SHOWS X-DIRECTION TOP LAYER ONLY.
2. EACH LAYER IS PLACED AS TWO ALTERNATE SETS: SET A (RED) & SET B (BLUE), EACH @ 300 mm -> COMBINED SPACING 150 mm.
3. TOP BARS ARE LAPPED ONLY AT MID-SPAN INSIDE THE HATCHED "TOP LAP ZONES". NO TOP LAPS OVER SUPPORTS.
4. LAP SPLICES SHALL BE STAGGERED AND NOT PROVIDED AT THE SAME SECTION: SET A & SET B LAPS ARE SEPARATED BY >= 800 mm.
5. LAP SPLICE LENGTH FOR ALL Ø12 mm BARS = 800 mm MINIMUM. LAPS LONGER THAN 800 mm SUIT THE 12 m STOCK - DO NOT CUT BARS.
6. ALL BARS ENDING AT SLAB EDGES & OPENINGS HAVE A 150 mm HOOK (TOP BARS TURNED DOWN). END COVER = 25 mm TYP., 50 mm WHERE THE BAR ENDS ON A BEAM / COLUMN.
7. NO REINFORCEMENT INSIDE LIFT CORE, STAIR, SLAB OPENINGS OR RAMP. AT THE CORE, BARS RUN THROUGH THE WALLS AND STOP AT THE INNER FACE (25 mm COVER + 150 HOOK).
8. VAR BARS: ONLY AT THE INCLINED SLAB EDGES; SHOWN BY A TYPICAL BAR PER ZONE - CUT LENGTHS IN THE VAR SCHEDULE.
9. SLAB DIMENSIONS & OPENINGS ARE AS PER STRUCTURAL PLAN. VERIFY ON SITE BEFORE CUTTING.
10. TRIMMER BARS AROUND OPENINGS AND RAMP REINFORCEMENT ARE AS PER STRUCTURAL DETAILS (NOT PART OF THIS SCHEDULE).
11. BAR LENGTHS IN THE SCHEDULE ARE CUTTING LENGTHS (INCLUDING HOOKS), IN METRES.

LEGEND

- SET A BAR (T12@300)
- SET B BAR (T12@300)
- PERMITTED LAP ZONE (MID-SPAN)
- DISTRIBUTION RANGE OF BAR GROUP
- T12@300 L=11.75 : BAR MARK / SPACING / CUT LENGTH

TYPICAL LAP & END DETAIL (N.T.S.)



SLAB / OPENING EDGE: COVER 25 mm - AT BEAMS: COVER 50 mm

CLIENT	ALOMNYAT COMPANY
PROJECT NAME	ALOMNYAT TOWERS

AL OMNYAT
REAL ESTATE AND TOURISM INVESTMENTS

INFORMATION	
Plot Area	2350 m^2
Building Are	2202 m^2
Coverage Area	
Number of Floors	27
Plot Number	
Approved By	

NOTES


ARCH. / MECH. / ELEC.	BAREEQ GENERAL CONTRACTING
Civil	CDEC CENTER OF DESIGN & ENGINEERING CONSULTING Prof. Dr. M. EL-ZANATY - Prof. Dr. A. EL-ZANATY
Main Contractor	HARMONIC FOR ENGINEERING & GENERAL CONTRACTING
Main Consultant	CREATIVE TOUCH FOR ENGINEERING & ARCHITECTURE CONSULTANCY

SHEET NAME

X-DIRECTION TOP REINFORCEMENT PLAN
Shop Drawing

SCALE	DATE
XX	19/10/2026

PROJECT NO.	REVISION	
K00	R01	ST-3

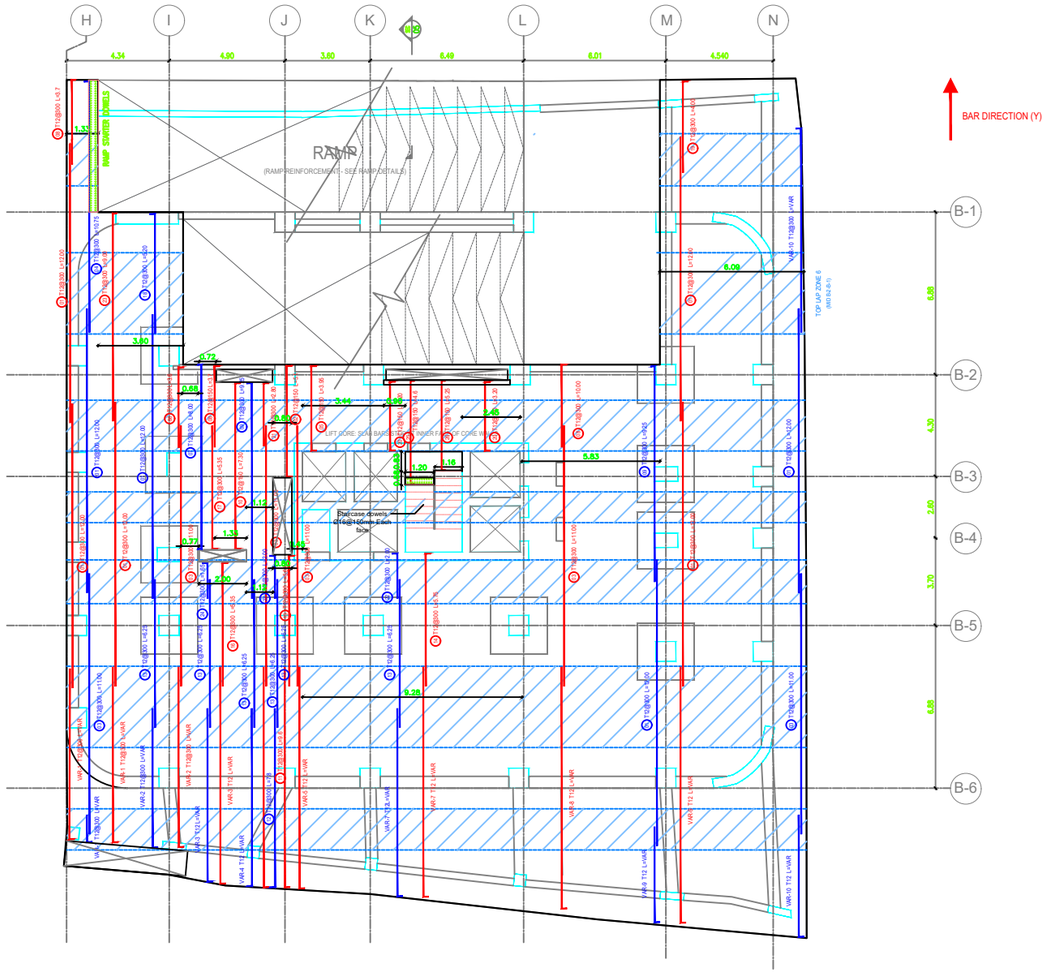

Y-DIRECTION TOP REINFORCEMENT PLAN

T12 @ 150 (SET A + SET B @ 300 EACH) - SCALE 1:100

BAR BENDING SCHEDULE - Y-DIRECTION TOP LAYER

NAME	BAR MARK	No.	Ø SIZE	LENGTH OF BAR (m)	SHAPE (m)
SLAB REINFORCEMENT Y-DIR TOP MESH (SETS A & B)	01	102	Ø12	12.00	12.00 — L = 12.00 (FULL CUT LENGTH)
	02	6	Ø12	5.1	0.15 — 4.8 — 0.15 — L = 11.40 (FULL CUT LENGTH)
	03	52	Ø12	11.00	11.00 — L = 11.00 (FULL CUT LENGTH)
	04	5	Ø12	10.75	10.60 — 0.15 — L = 10.75 (FULL CUT LENGTH)
	05	23	Ø12	3.87	0.15 — 3.57 — 0.15 — L = 10.30 (FULL CUT LENGTH)
	06	2	Ø12	3.6	3.45 — 0.15 — L = 10.25 (FULL CUT LENGTH)
	07	2	Ø12	8	0.15 — 7.7 — 0.15 — L = 10.05 (FULL CUT LENGTH)
	08	26	Ø12	3.7	3.55 — 0.15 — L = 10.00 (FULL CUT LENGTH)
	09	28	Ø12	9.6	9.30 — 0.15 — L = 9.25 (FULL CUT LENGTH)
	10	8	Ø12	7.3	0.15 — 7 — 0.15 — L = 7.30 (FULL CUT LENGTH)
	11	2	Ø12	9.45	9.3 — 0.15 — L = 6.80 (FULL CUT LENGTH)
	12	3	Ø12	7.65	7.5 — 0.15 — L = 6.70 (FULL CUT LENGTH)
	13	58	Ø12	6.25	6.25 — L = 6.25 (FULL CUT LENGTH)
	14	31	Ø12	5.75	5.60 — 0.15 — L = 5.75 (FULL CUT LENGTH)
	15	1	Ø12	5.65	5.50 — 0.15 — L = 5.65 (FULL CUT LENGTH)
	16	7	Ø12	5.35	5.20 — 0.15 — L = 5.35 (FULL CUT LENGTH)
	17	2	Ø12	5.35	0.15 — 5.20 — L = 5.35 (FULL CUT LENGTH)
	18	12	Ø12	5.20	5.05 — 0.15 — L = 5.20 (FULL CUT LENGTH)
	19	20	Ø12	3.2	2.9 — 0.15 — L = 4.00 (FULL CUT LENGTH)
	20	22	Ø12	3.15	0.15 — 2.85 — 0.15 — L = 3.20 (FULL CUT LENGTH)
	21	4	Ø12	2.80	2.65 — 0.15 — L = 2.80 (FULL CUT LENGTH)
	22	34	Ø12	2.00	1.85 — 0.15 — L = 2.05 (FULL CUT LENGTH)
	23	12	Ø12	9.00	0.15 — 8.85 — L = 9.00 (FULL CUT LENGTH)
	24	7	Ø12	1.65	1.50 — 0.15 — L = 1.65 (FULL CUT LENGTH)
	VAR	VAR	Ø12	VAR	0.15
	25	8	Ø12	4.04	4.34 — 0.15 — 0.15
	26	8	Ø12	4.05	0.15 — 3.75 — 0.15

GENERAL NOTES:

1. SLAB REINFORCEMENT: T12 @ 150 mm c/c IN BOTH X & Y DIRECTIONS AT TOP & BOTTOM LAYERS. THIS SHEET SHOWS Y-DIRECTION TOP LAYER ONLY.
2. EACH LAYER IS PLACED AS TWO ALTERNATE SETS: SET A (RED) & SET B (BLUE), EACH @ 300 mm -> COMBINED SPACING 150 mm.
3. TOP BARS ARE LAPPED ONLY AT MID-SPAN INSIDE THE HATCHED "TOP LAP ZONES". NO TOP LAPS OVER SUPPORTS.
4. LAP SPLICES SHALL BE STAGGERED AND NOT PROVIDED AT THE SAME SECTION: SET A & SET B LAPS ARE SEPARATED BY >= 800 mm.
5. LAP SPLICE LENGTH FOR ALL Ø12 mm BARS = 800 mm MINIMUM. LAPS LONGER THAN 800 mm SUIT THE 12 m STOCK - DO NOT CUT BARS.
6. ALL BARS ENDING AT SLAB EDGES & OPENINGS HAVE A 150 mm HOOK (TOP BARS TURNED DOWN). END COVER = 25 mm TYP., 50 mm WHERE THE BAR ENDS ON A BEAM / COLUMN.
7. NO REINFORCEMENT INSIDE LIFT CORE, STAIR, SLAB OPENINGS OR RAMP. AT THE CORE, BARS RUN THROUGH THE WALLS AND STOP AT THE INNER FACE (25 mm COVER + 150 HOOK).
8. VAR BARS: ONLY AT THE INCLINED SLAB EDGES; SHOWN BY A TYPICAL BAR PER ZONE - CUT LENGTHS IN THE VAR SCHEDULE.
9. SLAB DIMENSIONS & OPENINGS ARE AS PER STRUCTURAL PLAN. VERIFY ON SITE BEFORE CUTTING.
10. TRIMMER BARS AROUND OPENINGS AND RAMP REINFORCEMENT ARE AS PER STRUCTURAL DETAILS (NOT PART OF THIS SCHEDULE).
11. BAR LENGTHS IN THE SCHEDULE ARE CUTTING LENGTHS (INCLUDING HOOKS), IN METRES.

LEGEND

- SET A BAR (T12@300)
- SET B BAR (T12@300)
- PERMITTED LAP ZONE (MID-SPAN)
- DISTRIBUTION RANGE OF BAR GROUP
- T12@300 L=11.75 : BAR MARK / SPACING / CUT LENGTH

TYPICAL LAP & END DETAIL (N.T.S.)



SLAB / OPENING EDGE: COVER 25 mm - AT BEAMS: COVER 50 mm

CLIENT	ALOMNYAT COMPANY
PROJECT NAME	ALOMNYAT TOWERS

AL OMNYAT
REAL ESTATE AND TOURISM INVESTMENTS


INFORMATION	
Plot Area	2350 m²
Building Are	2202 m²
Coverage Area	
Number of Floors	27
Plot Number	
Approved By	

NOTES

ARCH.	BAREEQ GENERAL CONTRACTING
MECH.	
ELEC.	
Civil	CDEC — CENTER OF DESIGN & ENGINEERING CONSULTING — Prof. Dr. M. EL-ZANATY - Prof. Dr. A. EL-ZANATY — Administration Building N0.(2) Spring Valley(Ramsis) AL-Motamayaz district 6 th of October-Giza
Main Contractor	HARMONIC FOR ENGINEERING & GENERAL CONTRACTING
Main Consultant	CREATIVE TOUCH FOR INTERIOR DESIGN & FINE ENGINEERING

SHEET NAME	
Y-DIRECTION TOP REINFORCEMENT PLAN Shop Drawing	
SCALE XX	DATE 19/10/2026
PROJECT NO. K00	REVISION R01


ST-4

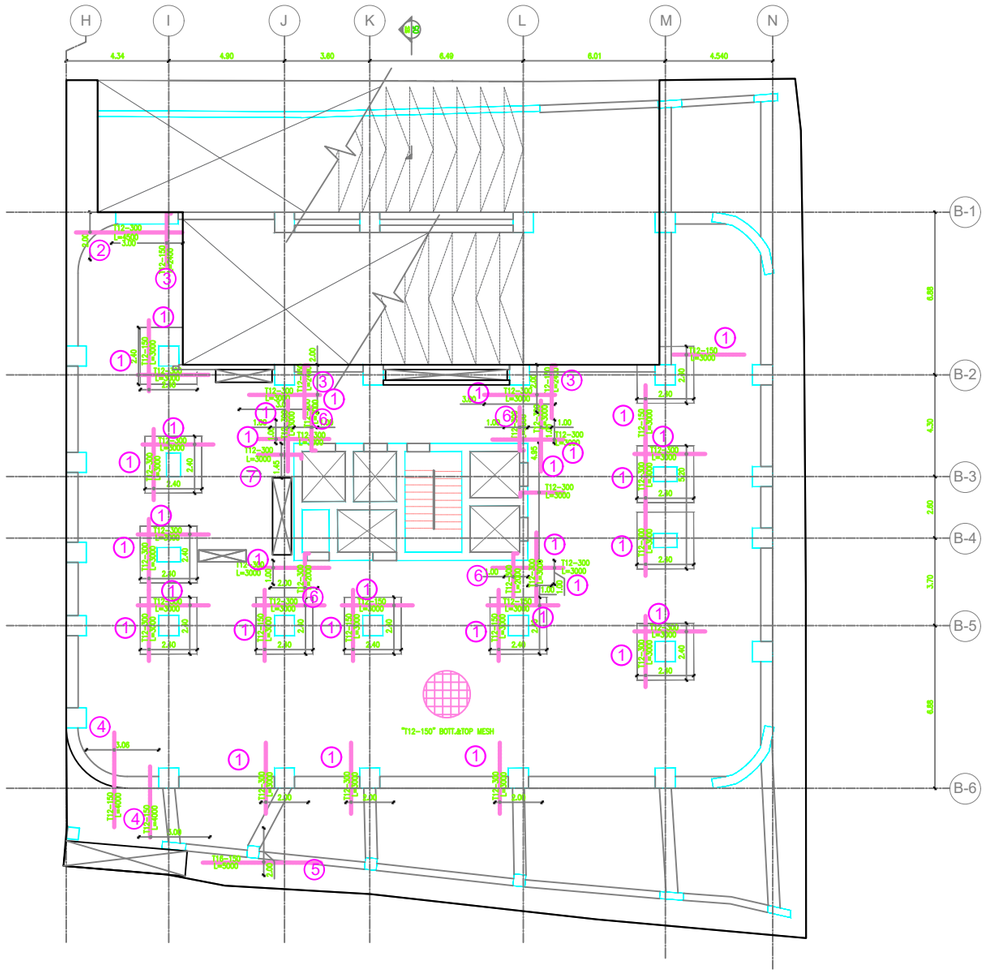

BAR BENDING SCHEDULE

Bar Mark	Name	No.	Ø size	LENGTH OF BAR	SHAPE
1	Additional	323	Ø12	3 m	
2		14	Ø12	4.5m	
3		74	Ø12	2.4 m	0.15 2.25 m
4		41	Ø12	4 m	
5		14	Ø16	5 m	
6		34	Ø12	2 m	0.15 1.85 m
7		54	Ø12	3m	0.15 2.85 m

CLIENT	AL OMNYAT REAL ESTATE AND TOURISM INVESTMENTS	INFORMATION	NOTES	ARCH. MECH. ELEC.	BAREEQ GENERAL CONTRACTING
ALOMNYAT COMPANY		Plot Area 2350 m^2		Civil	CDEC CENTER OF DESIGN & ENGINEERING CONSULTING
PROJECT NAME		Building Are 2202 m^2		Main Contractor	HARMONIC FOR ENGINEERING & GENERAL CONTRACTING
ALOMNYAT TOWERS		Coverage Area		Main Consultant	CREATIVE TOUCH
		Number of Floors 27		SHEET NAME	Additional & drop panel Rebar Of Shop Drawing
		Plot Number		SCALE XX	DATE 19/10/2026
		Approved By		PROJECT NO. K00	REVISION R01
					ST-5

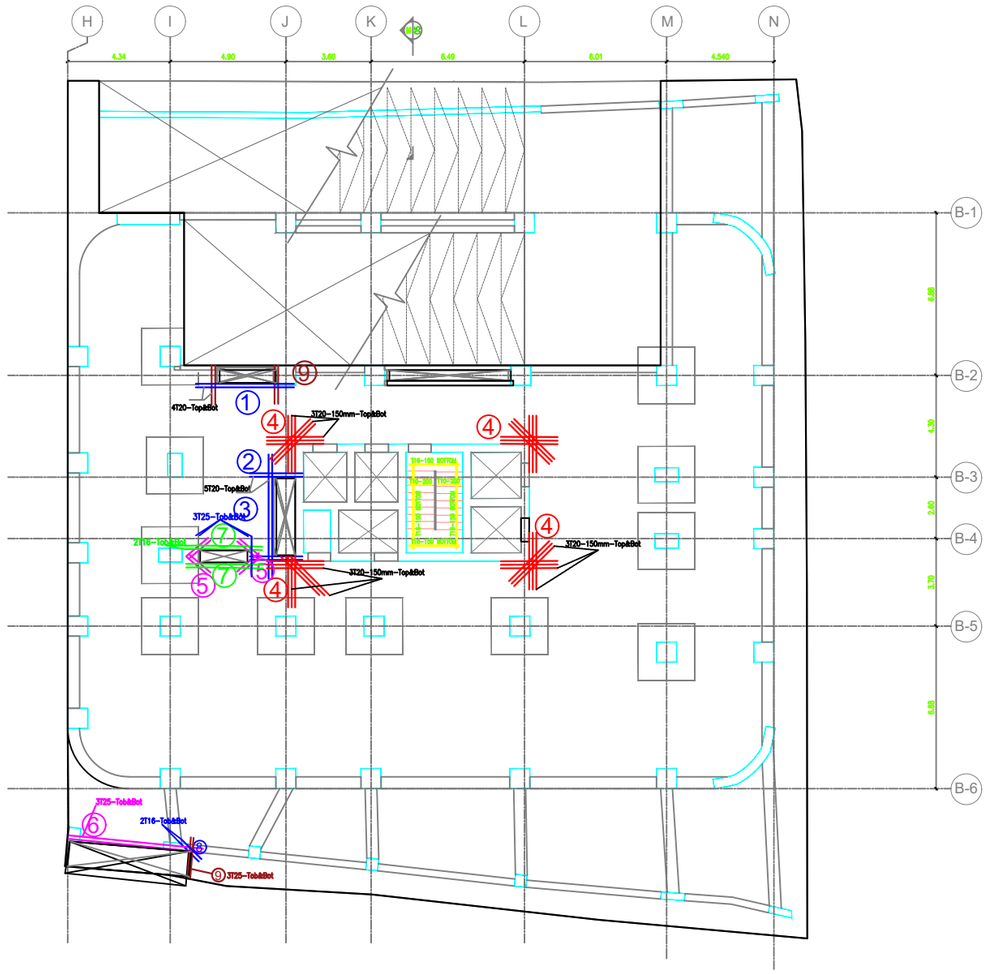

BAR BENDING SCHEDULE


Bar Mark	No.	Ø size	LENGTH OF BAR	SHAPE
1	8	Ø20	4.2 m	
2	20	Ø20	2.5 m	
3	10	Ø20	5.25 m	
4	72	Ø20	2.5 m	
5	24	Ø16	1.2 m	
6	6	Ø25	6 m	
7	8	Ø16	3.5 m	
8	4	Ø16	2.00 m	
9	22	Ø25	1.7 m	
10	12	Ø25	3.5 m	

CLIENT	AL OMNYAT REAL ESTATE AND TOURISM INVESTMENTS	INFORMATION	NOTES (UNLESS NOTED)	ARCH. MECH. ELEC.	BAREEQ GENERAL CONTRACTING	Main Contractor	HARMONIC FOR ENGINEERING & GENERAL CONTRACTING
ALOMNYAT COMPANY		Plot Area 2350 m^2					
PROJECT NAME		Building Are 2202 m^2					
ALOMNYAT TOWERS		Coverage Area		Civil	CDEC CENTER OF DESIGN & ENGINEERING CONSULTING Prof. Dr. M. EL-ZANATY - Prof. Dr. A. EL-ZANATY	Main Consultant	CREATIVE TOUCH
		Number of Floors 27					
		Plot Number					
		Approved By					


SHEET NAME	
Shaft -Slab Reinforcement Shop Drawing	
SCALE XX	DATE 19/10/2026
PROJECT NO. K00	REVISION R01

ST-6


TYPE C
typical detials

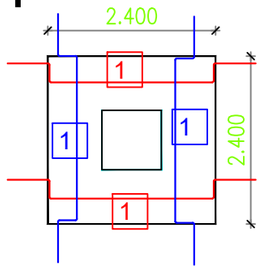


TYPE D

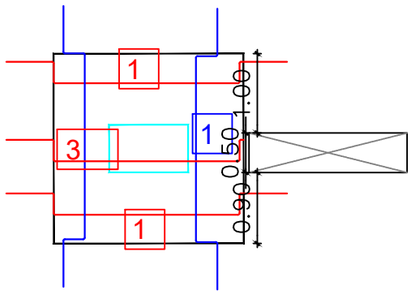








TYPE E

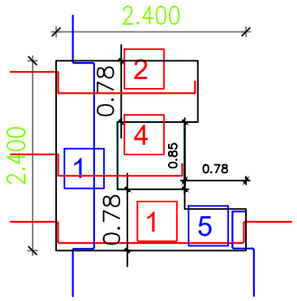

TYPE F

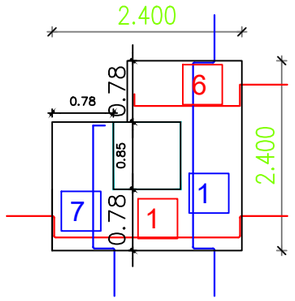

BAR BENDING SCHEDULE

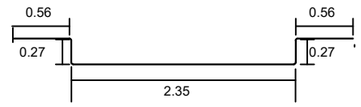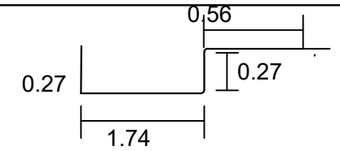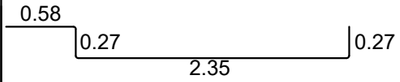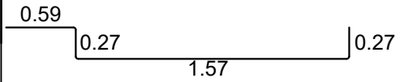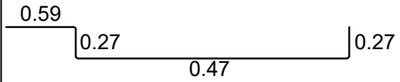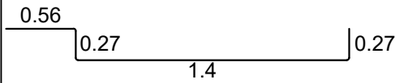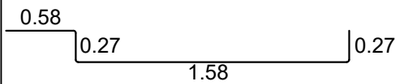
Bar Mark	No.	Ø size	LENGTH OF BAR	SHAPE
1	96	Ø12	4.1 m	
2	6	Ø12	2.75 m	
3	4	Ø12	3.80 m	
4	8	Ø12	2.7 m	
5	6	Ø12	1.6 m	
6	7	Ø12	2.5 m	
7	7	Ø12	2.7 m	

All Drop panle Reinforcement T12 @150mm

CLIENT	AL OMNYAT REAL ESTATE AND TOURISM INVESTMENTS	INFORMATION	NOTES	ARCH.	BAREEQ GENERAL CONTRACTING	Main Contractor	HARMONIC FOR ENGINEERING & GENERAL CONTRACTING
ALOMNYAT COMPANY		Plot Area 2350 m^2		MECH.			
PROJECT NAME		Building Are 2202 m^2		ELEC.		Main Consultant	CREATIVE TOUCH
ALOMNYAT TOWERS		Coverage Area		Civil	CDEC CENTER OF DESIGN & ENGINEERING CONSULTING Prof. Dr. M. EL-ZANATY - Prof. Dr. A. EL-ZANATY		
		Number of Floors 27					
		Plot Number					
		Approved By					

SHEET NAME	
Drop panle Reinforcement Shop Drawing	
SCALE XX	DATE 19/10/2026
PROJECT NO. K00	REVISION R01

ST-7

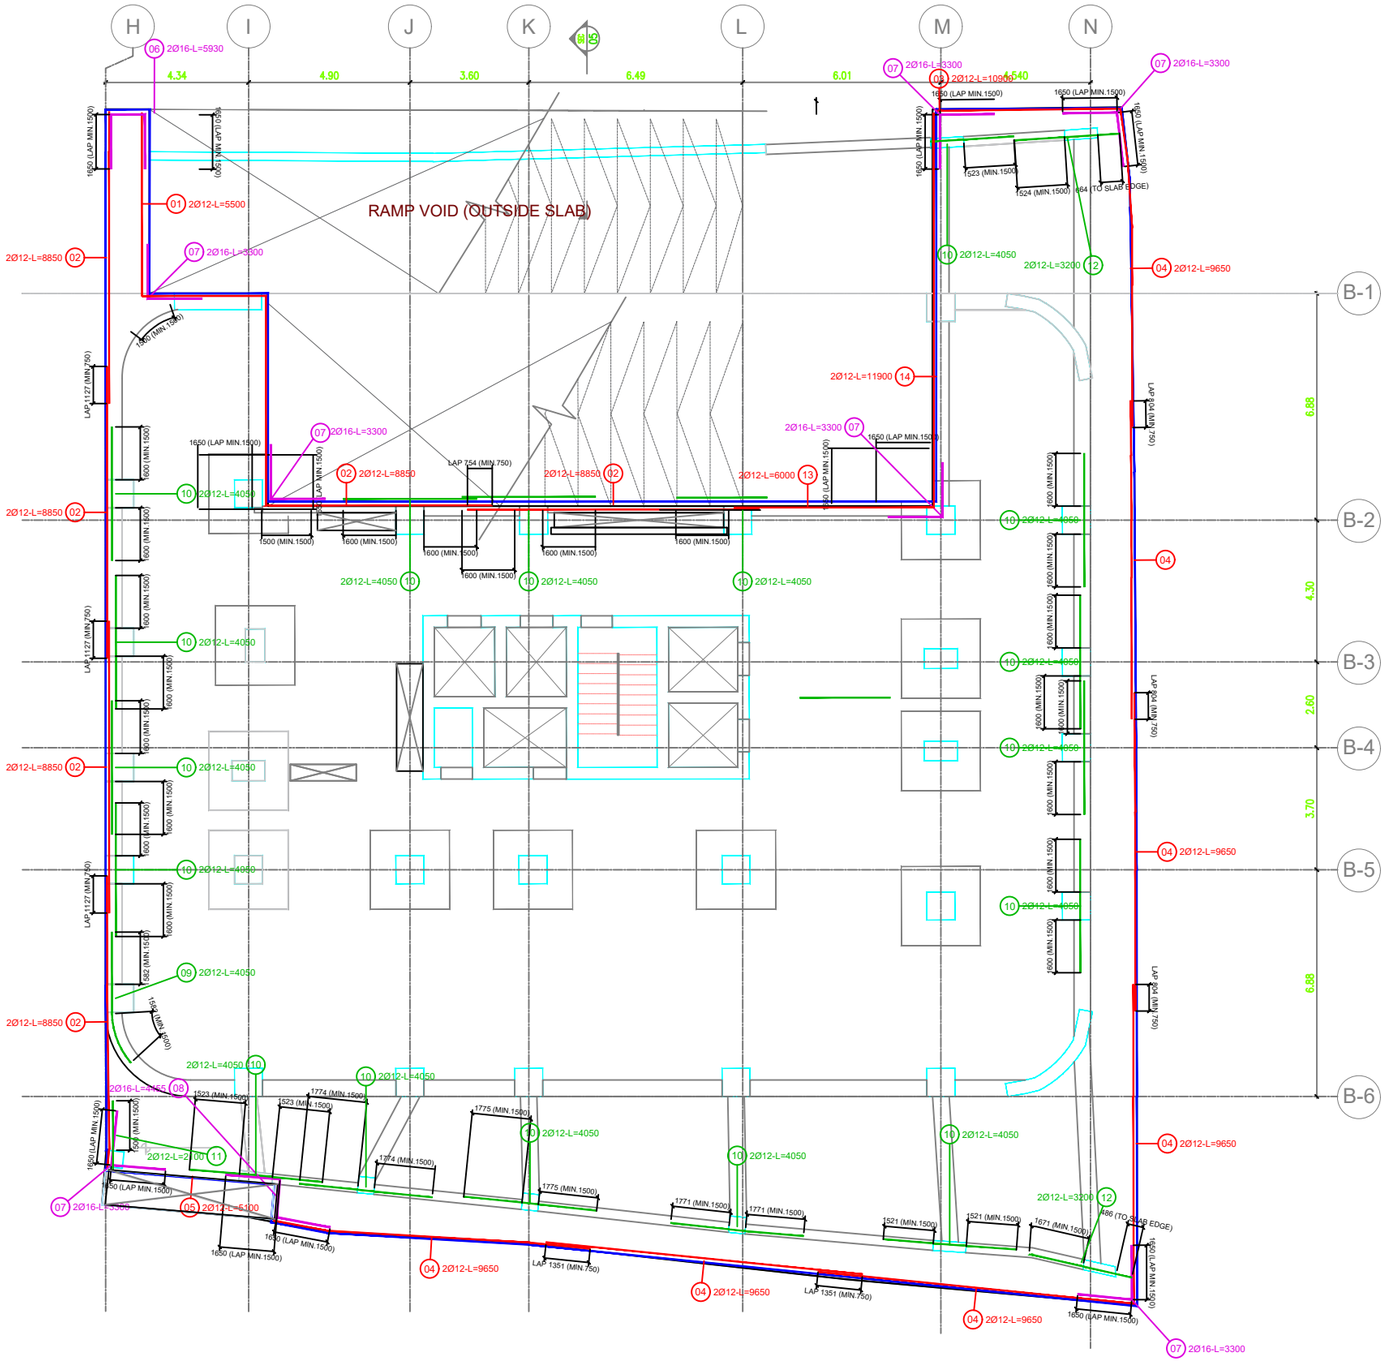

STABILITY TIES PLAN - NOTES 6.1 / 6.3 / 6.4 (TYPICAL FLOOR)

SCALE 1:100 - UNITS: m - BAR LENGTHS IN mm - SAME COORDINATES AS ARCHITECTURAL / STRUCTURAL SLAB PLAN

- STRUCTURAL SLAB BOUNDARY (INCL. CANTILEVERS)
- OPENING (X) - NO TIE BAR CROSSES AN OPENING
- NOTE 6.1 - PERIPHERAL TIE 2Ø12, AXIS 75 mm FROM SLAB EDGE, LAP >= 750
- NOTE 6.3 - CORNER BAR 2Ø16 (L / U / Z), EACH LEG LAPPED >= 1500 WITH 6.1
- NOTE 6.4 - 2Ø12 STRAIGHT BARS THROUGH EXTERNAL COLUMNS / WALL, >= 1500 EACH SIDE
- LIMITS OF LAP ZONE BETWEEN 6.1 BARS


CLIENT	
ALOMNYAT COMPANY	AL OMNYAT REAL ESTATE AND TOURISM INVESTMENTS
PROJECT NAME	
ALOMNYAT TOWERS	


INFORMATION	NOTES
Plot Area 2350 m^2	
Building Are 2202 m^2	
Coverage Area	
Number of Floors 27	
Plot Number	
Approved By	

ARCH. / MECH. / ELEC.	BAREEQ GENERAL CONTRACTING
Civil	CDEC CENTER OF DESIGN & ENGINEERING CONSULTING Prof. Dr. M. EL-ZANATY - Prof. Dr. A. EL-ZANATY
Main Contractor	HARMONIC FOR ENGINEERING & GENERAL CONTRACTING
Main Consultant	CREATIVE TOUCH FOR DESIGN & GENERAL CONTRACTING

SHEET NAME	
STABILITY TIES REINFORCEMENT PLAN LAYOUT	
SCALE XX	DATE 19/10/2026
PROJECT NO. K00	REVISION R01

ST-8

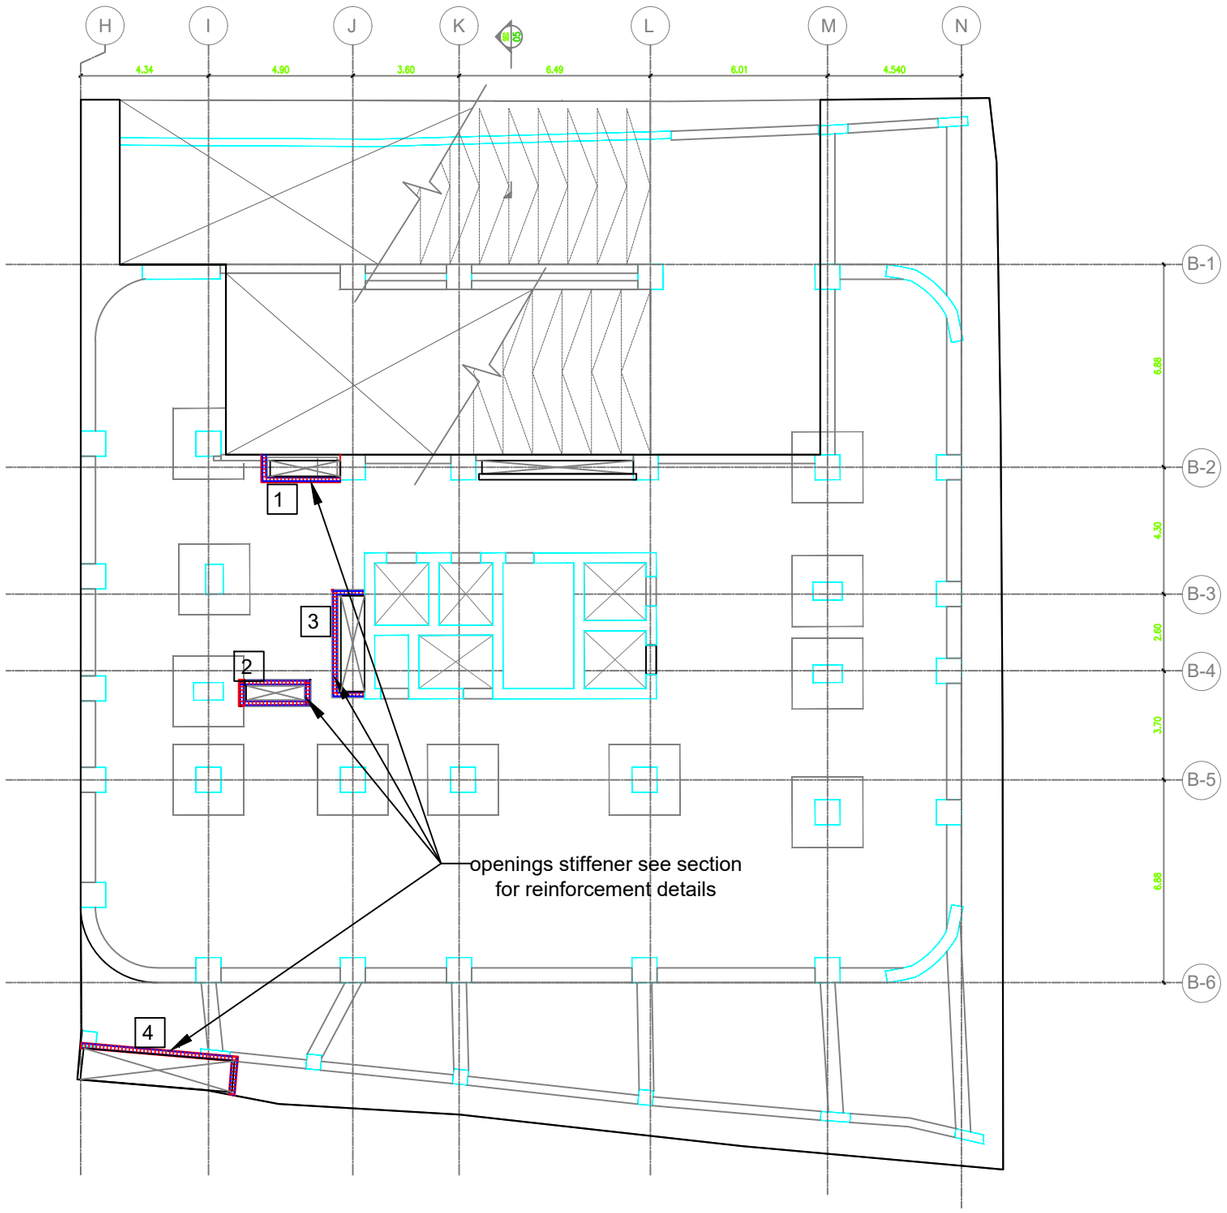

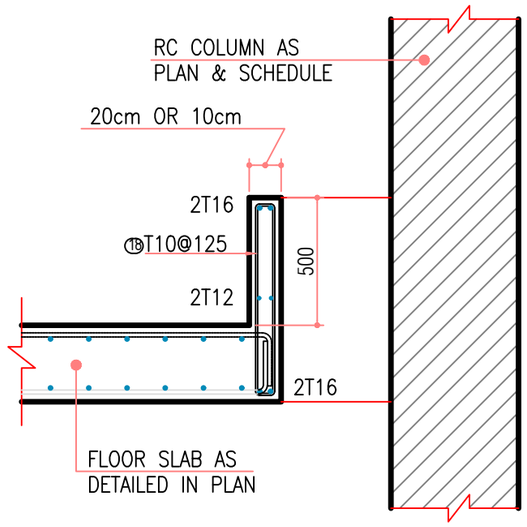

Openings Stiffeners section details

NOTE:-
OPENING STIFFENERS 3,4 WHIDTH 20CM
OPENING STIFFENERS 1,2 WHIDTH 10CM

CLIENT	AL OMNYAT REAL ESTATE AND TOURISM INVESTMENTS	INFORMATION	NOTES	ARCH.	BAREEQ GENERAL CONTRACTING	Main Contractor	HARMONIC FOR ENGINEERING & GENERAL CONTRACTING
ALOMNYAT COMPANY		Plot Area 2350 m^2		MECH.			
PROJECT NAME		Building Are 2202 m^2		ELEC.		Main Consultant	CREATIVE TOUCH FOR DESIGN & GENERAL TRADE & CONTRACTING
ALOMNYAT TOWERS		Coverage Area		Civil	CDEC CENTER OF DESIGN & ENGINEERING CONSULTING Prof. Dr. M. EL-ZANATY - Prof. Dr. A. EL-ZANATY		
		Number of Floors 27					
		Plot Number					
		Approved By					

SHEET NAME	
OPENING STIFFENER DETAIL	
SCALE XX	DATE 19/10/2026
PROJECT NO. K00	REVISION R01

ST-9